


ERICSSON SOFTWARE CAMPUS

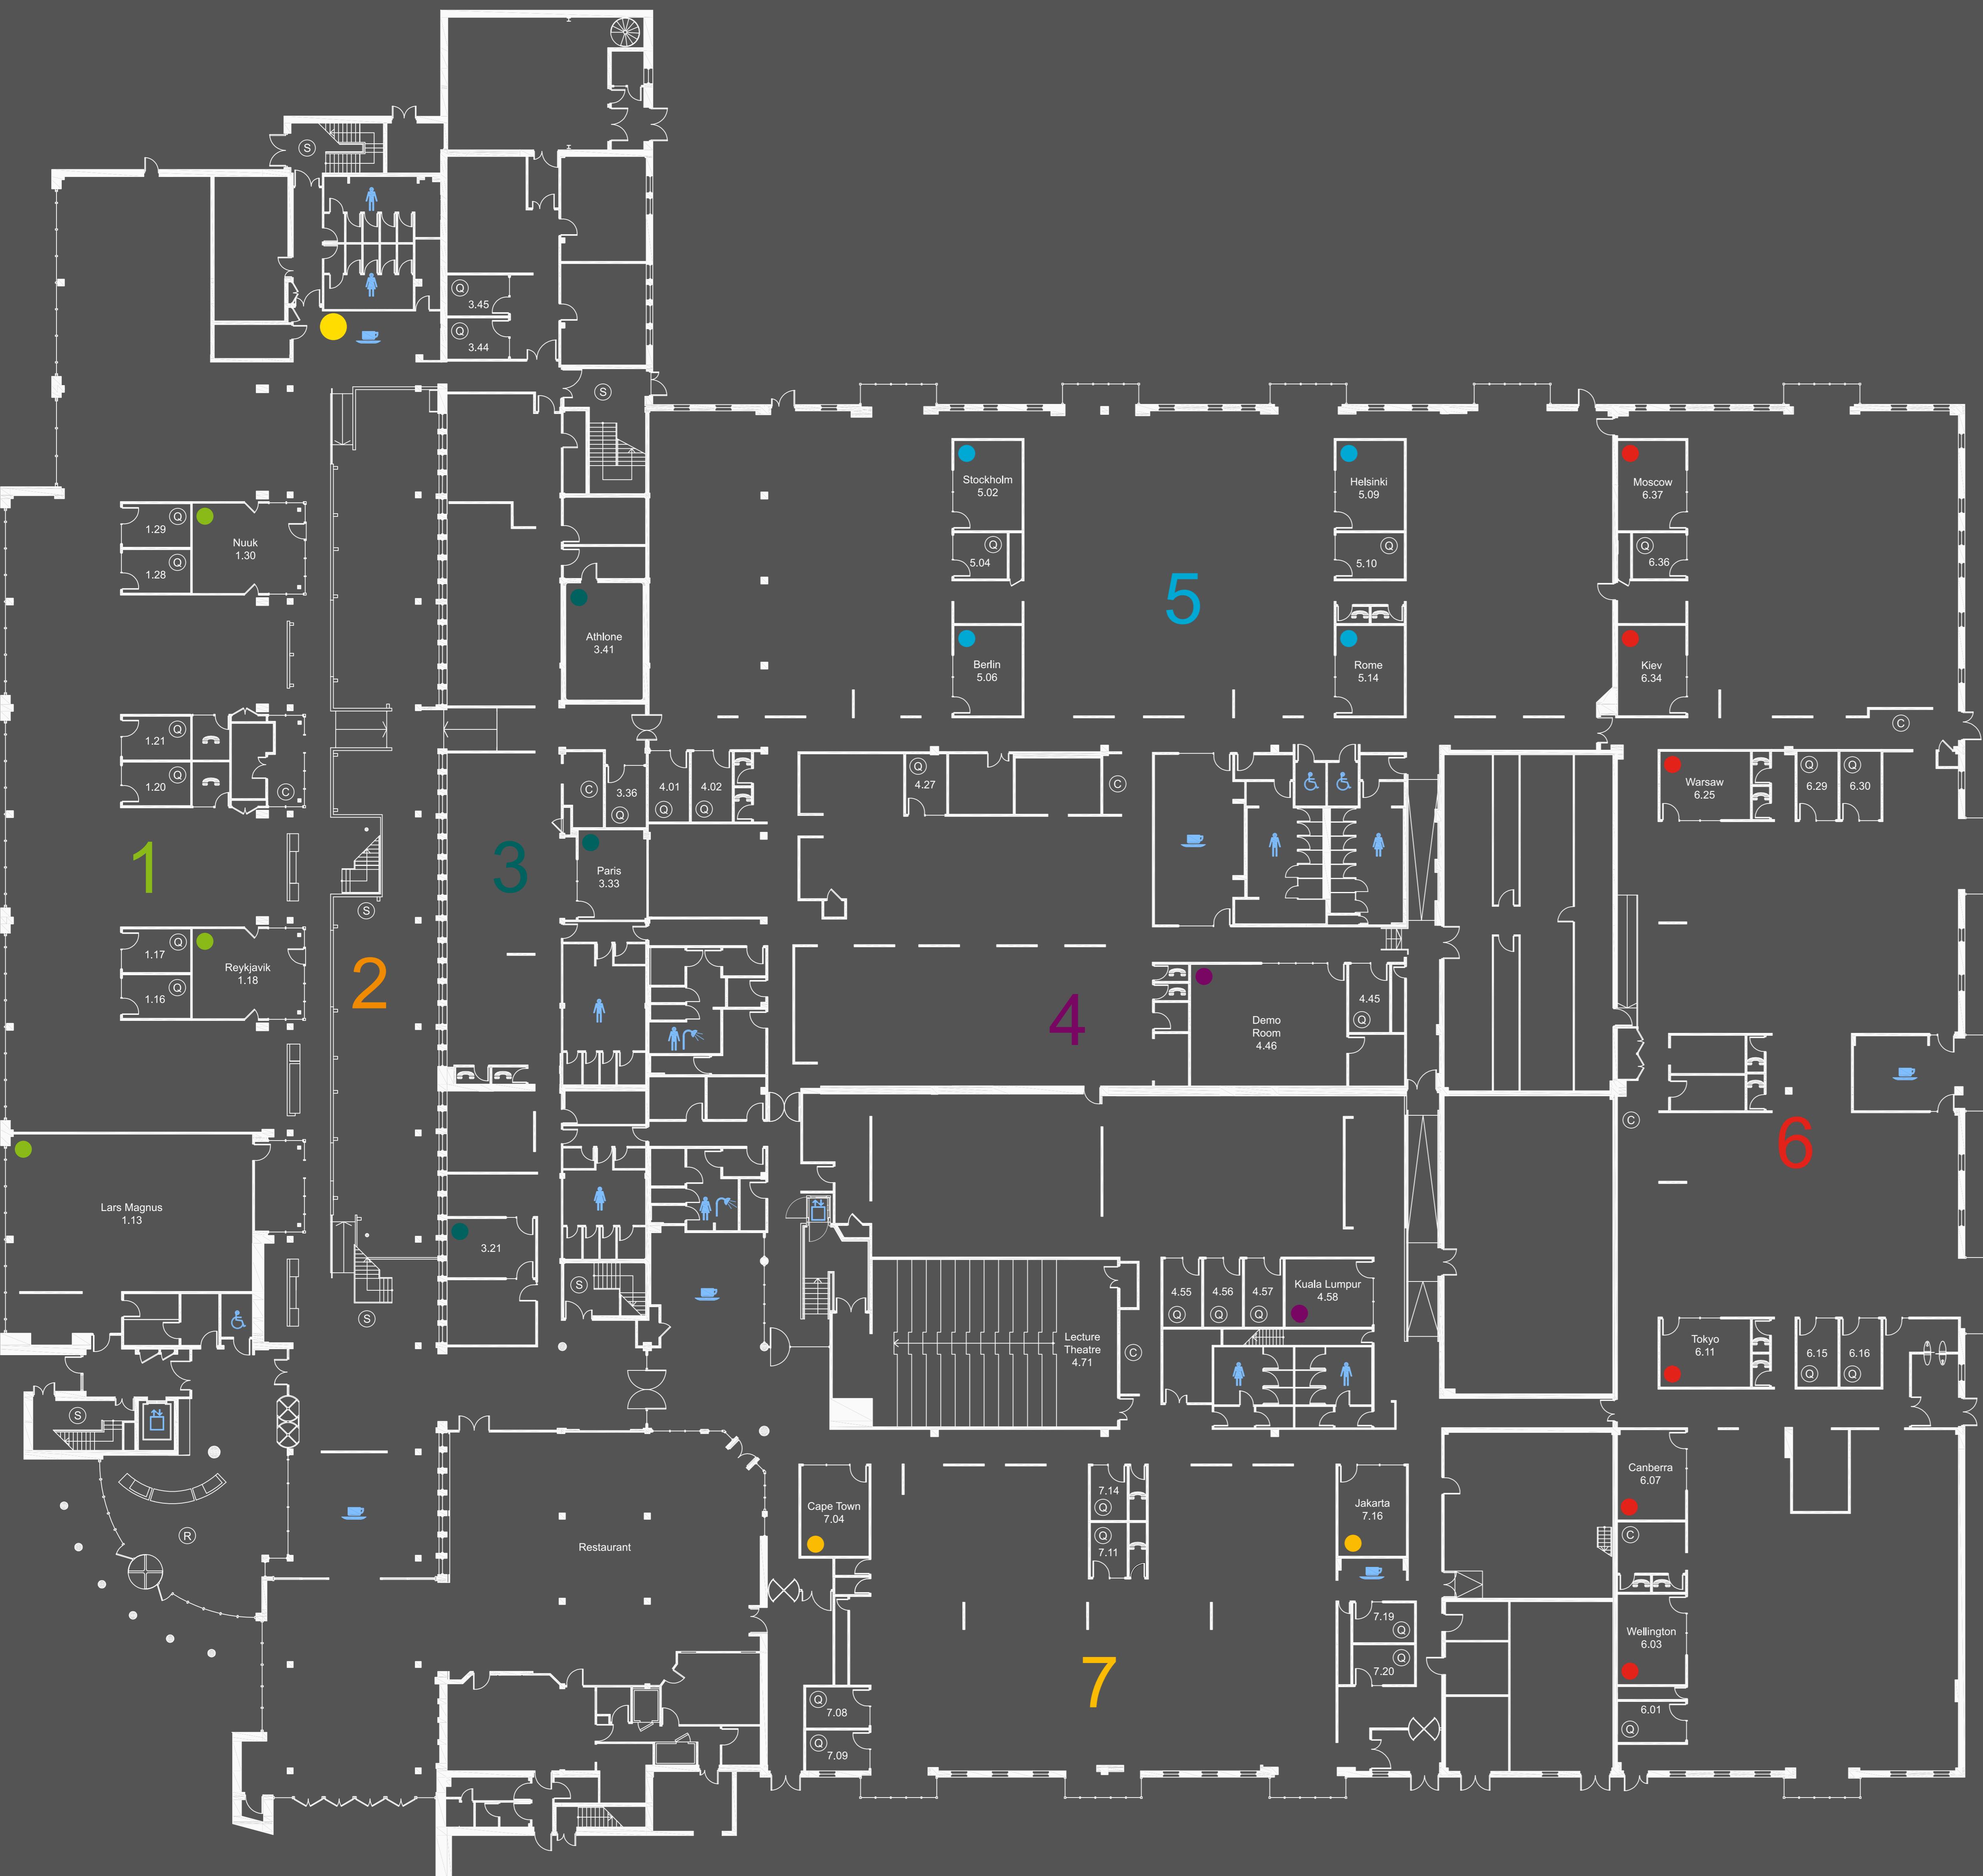

GROUND FLOOR

LEGEND

- (R) Reception
- (S) Stairwell
- (Q) Quiet Room
- (C) Print / Copy
- (T) Telephone Booths
- (Cup) Break Out Area
- (Male/Female) Male WC
- (Disabled) Disabled WC
- (Male/Female Changing) Male Changing
- (Female Changing) Female Changing
- (Up/Down) Lifts


Meeting / Other Rooms

ZONE 1	Lars Magnus 1.13
	Reykjavik 1.18
	Nuuk 1.30
ZONE 3	Paris 3.33
ZONE 4	Demo Room 4.46
	Kuala Lumpur 4.58
ZONE 5	Stockholm 5.02
	Berlin 5.06
	Helsinki 5.09
	Rome 5.14
ZONE 6	Wellington 6.03
	Canberra 6.07
	Tokyo 6.11
	Warsaw 6.25
	Kiev 6.34
	Moscow 6.37
ZONE 7	Cape Town 7.04
	Jakarta 7.16
ZONE 8	Honolulu 8.13
	Ottawa 8.24
	Anchorage 8.39
ZONE 9	Buenos Aires 9.05
	Brasilia 9.24
	Washington DC 9.38
	V.A. Lab 9.46

Conference / Telepresence Room


ZONE 3	Athlone 3.41
--------	--------------

YOU ARE HERE

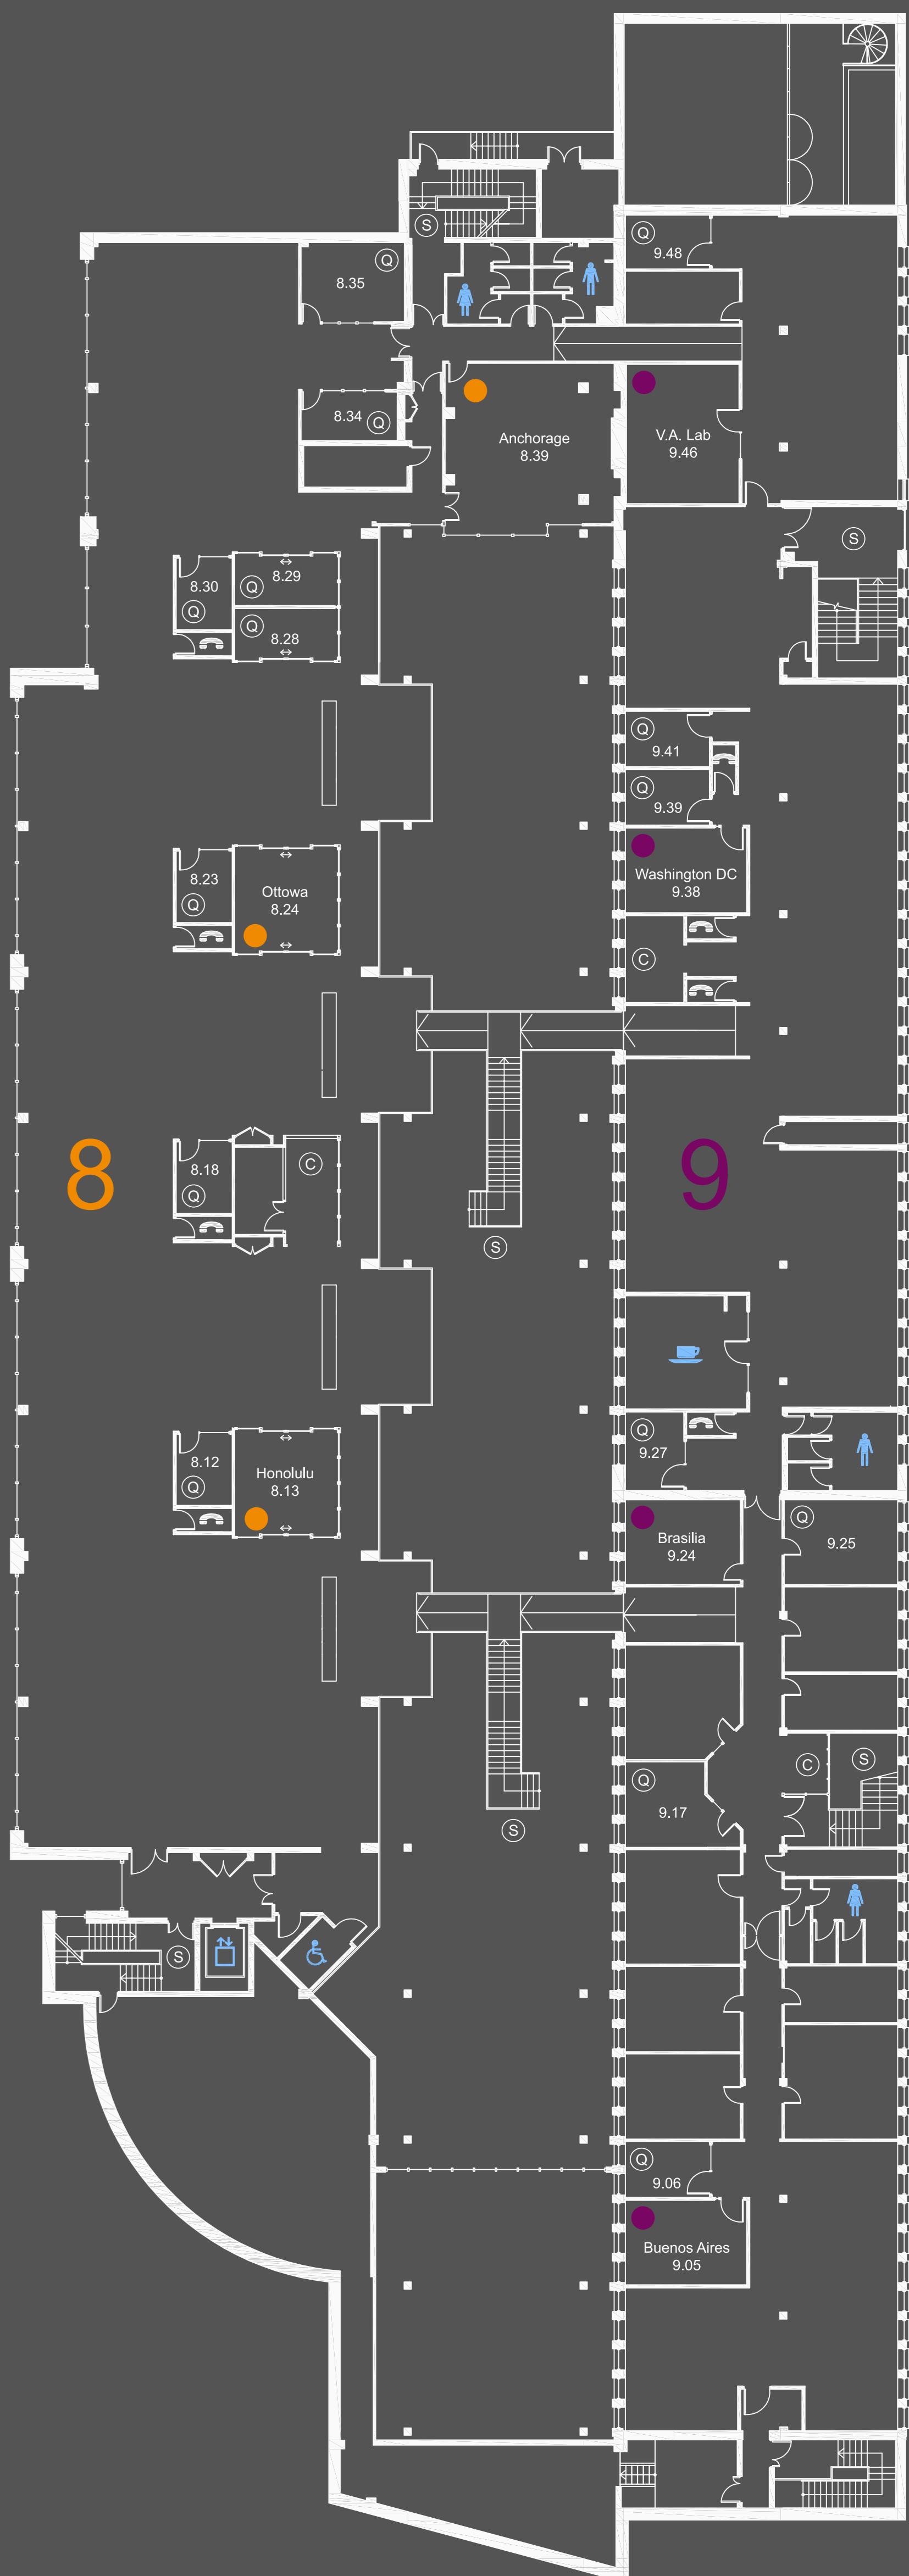


FIRST FLOOR

ERICSSON SOFTWARE CAMPUS

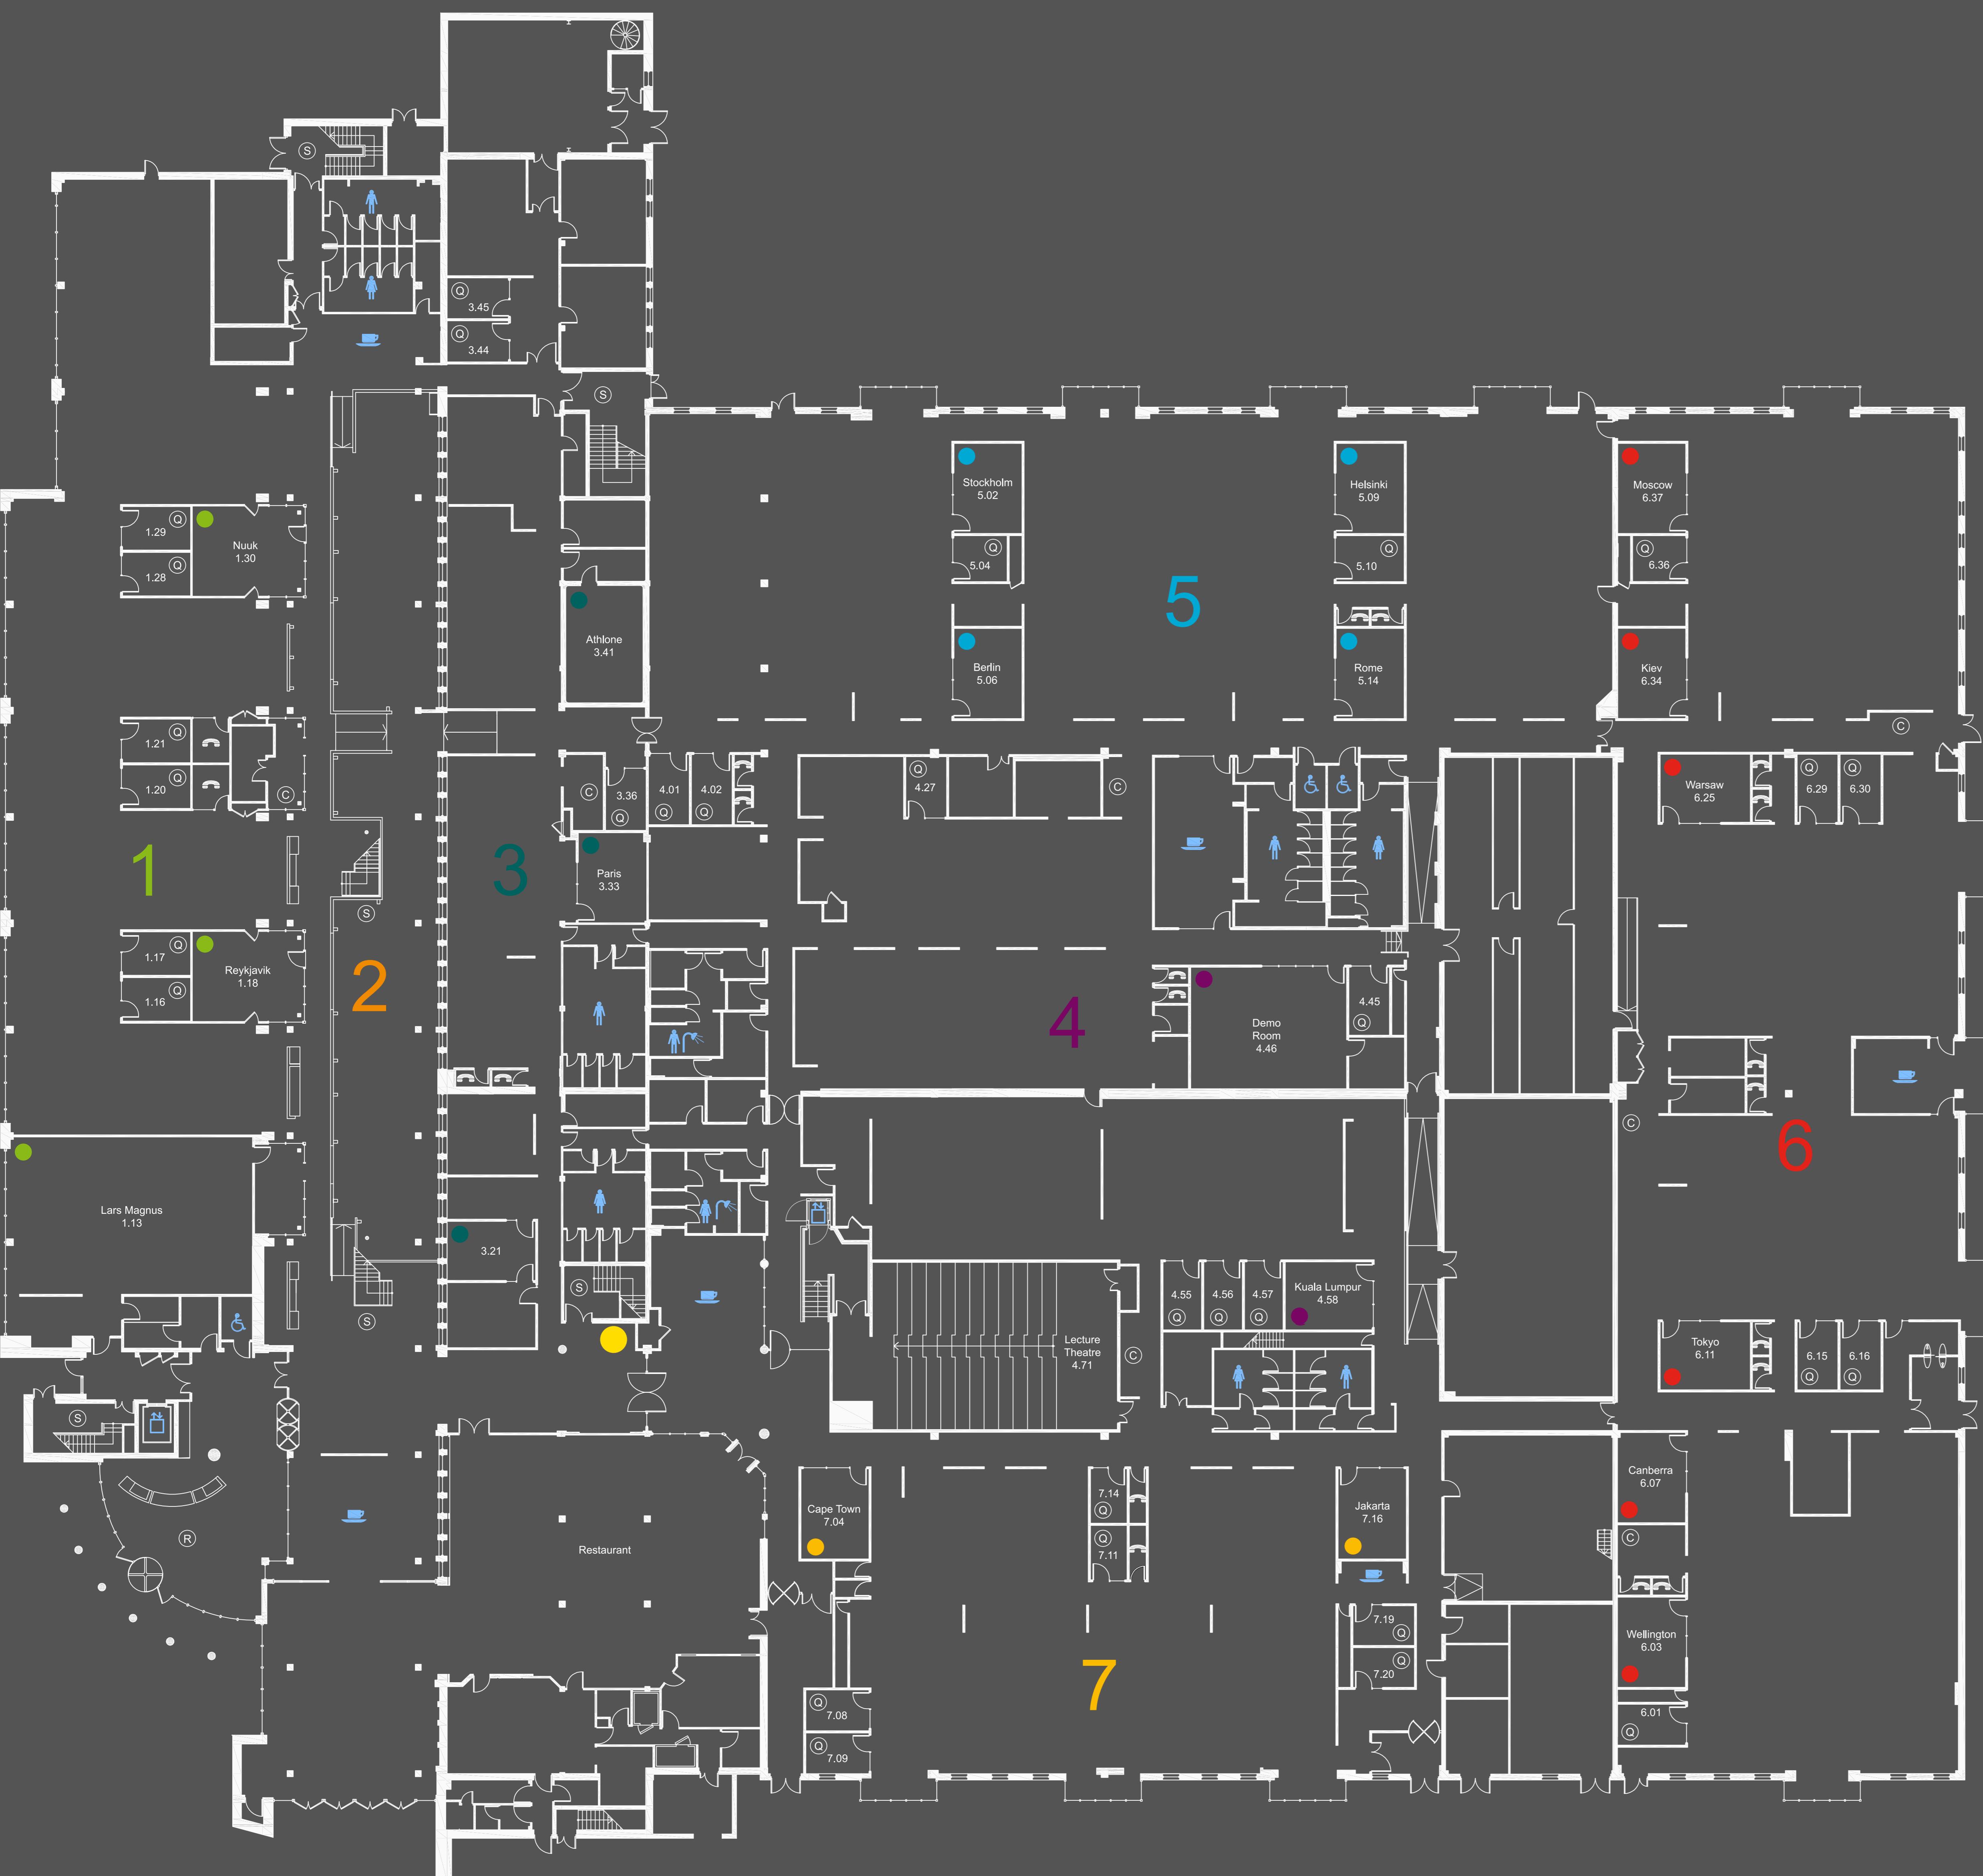

GROUND FLOOR

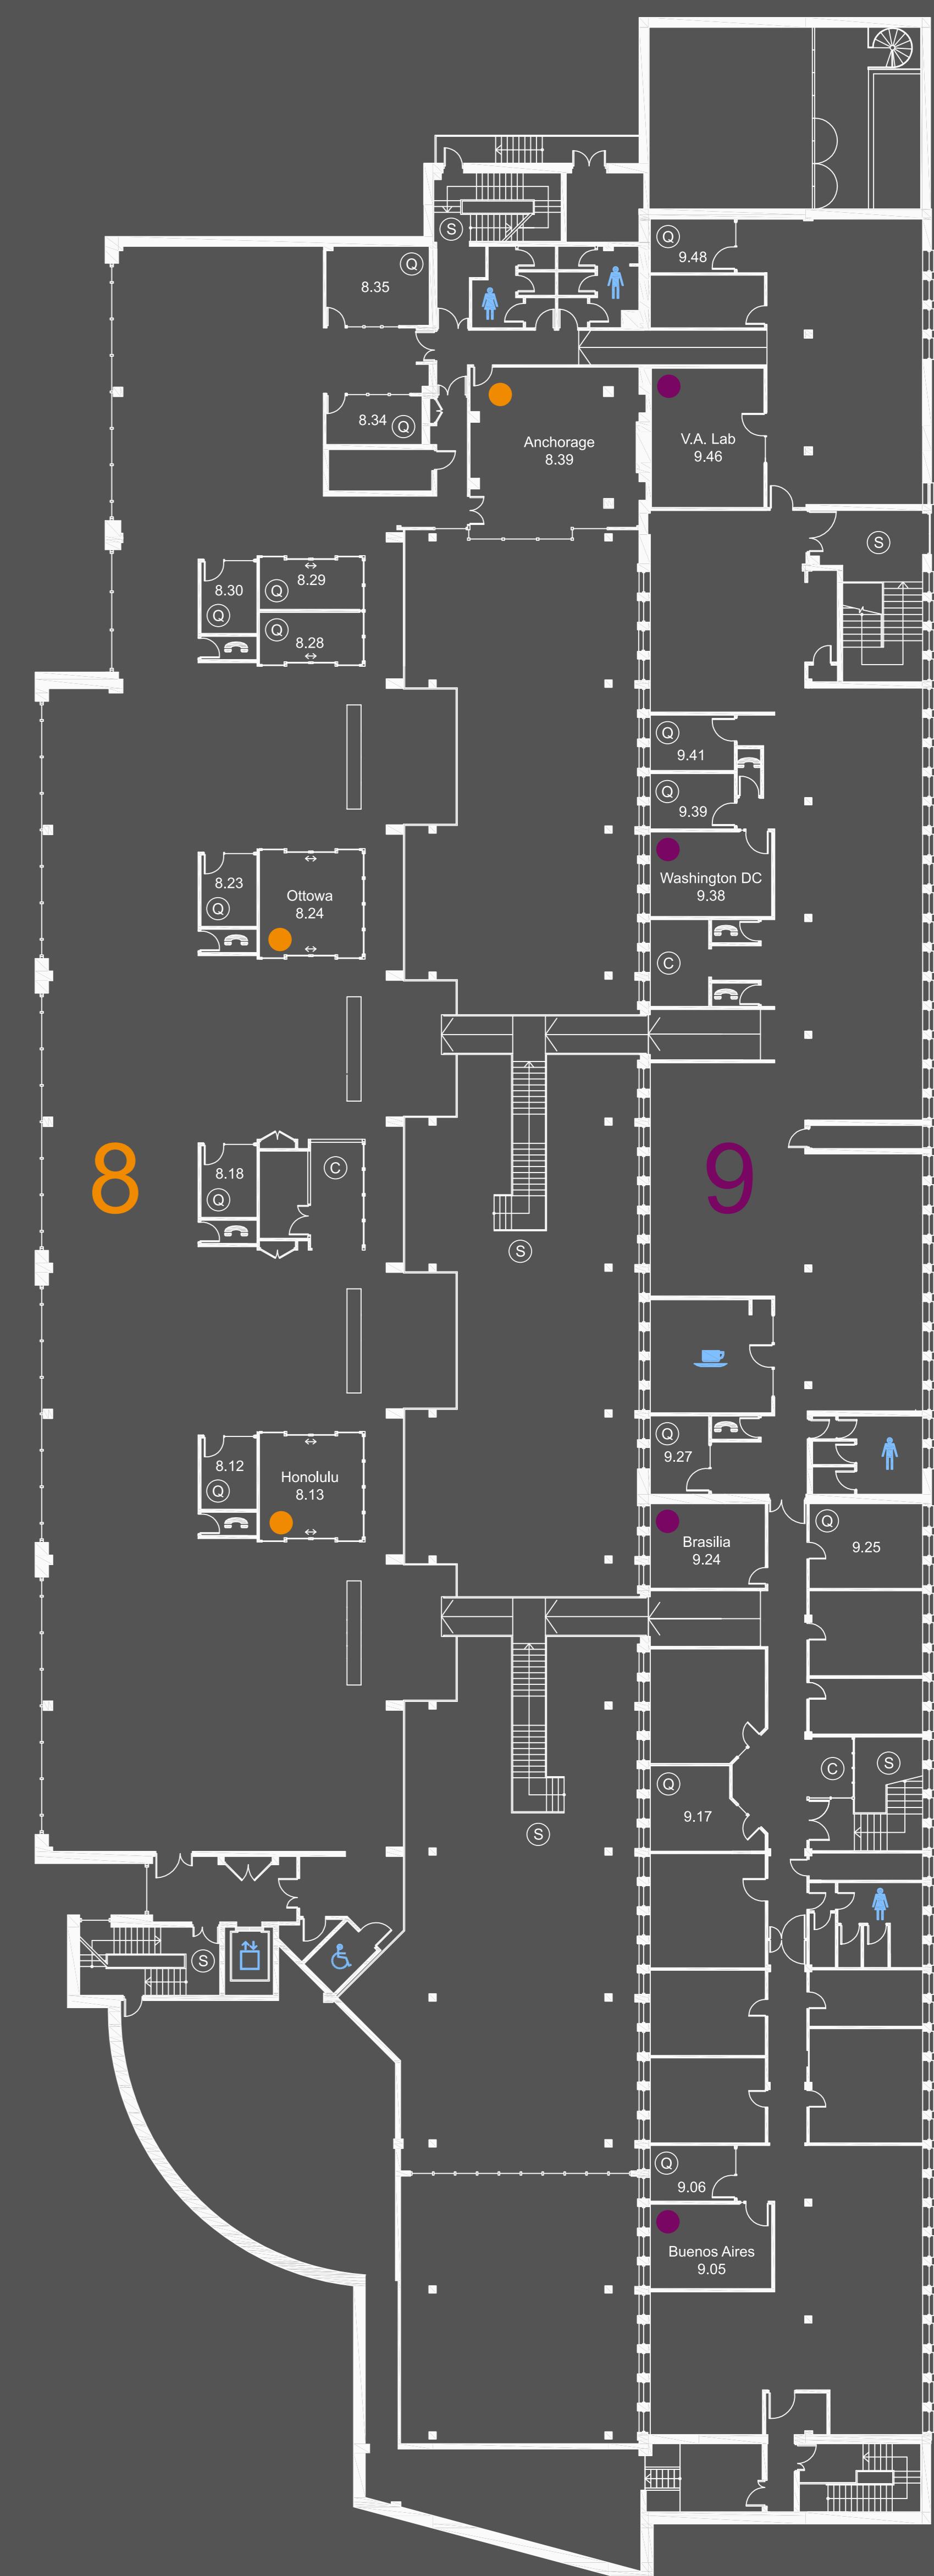


FIRST FLOOR

ERICSSON SOFTWARE CAMPUS



GROUND FLOOR

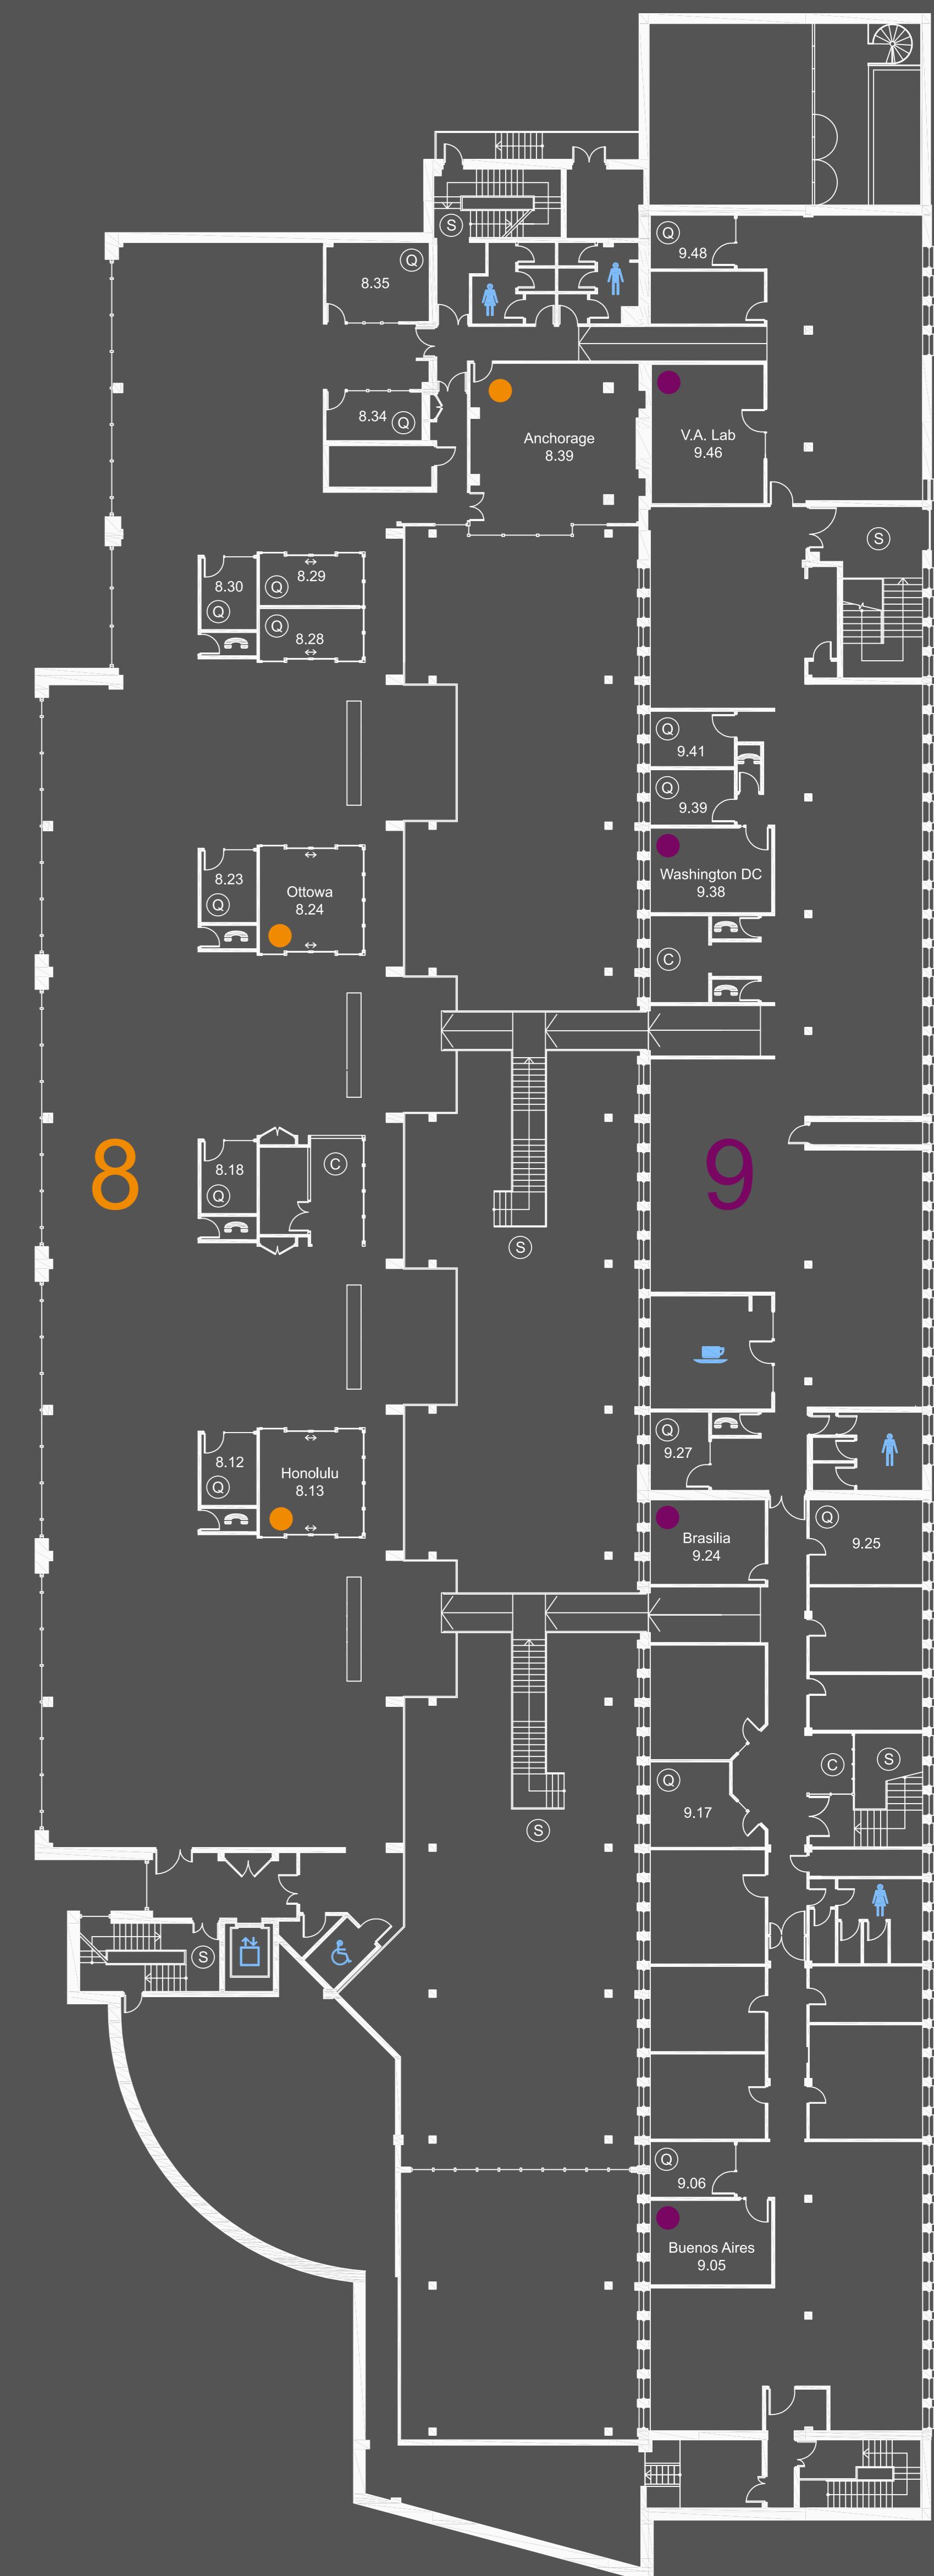

FIRST FLOOR

ERICSSON SOFTWARE CAMPUS



GROUND FLOOR

LEGEND

- (R) Reception
- (S) Stairwell
- (Q) Quiet Room
- (C) Print / Copy
- (T) Telephone Booths
- (Cup) Break Out Area
- (Male/Female) Male WC
- (Disabled) Female WC
- (Male/Female Changing) Male Changing
- (Female Changing) Female Changing
- (Up/Down) Lifts


Meeting / Other Rooms

ZONE 1	
Lars Magnus	1.13
Reykjavik	1.18
Nuuk	1.30
ZONE 3	
Paris	3.33
ZONE 4	
Demo Room	4.46
Kuala Lumpur	4.58
ZONE 5	
Stockhom	5.02
Berlin	5.06
Helsinki	5.09
Rome	5.14
ZONE 6	
Wellington	6.03
Canberra	6.07
Tokyo	6.11
Warsaw	6.25
Kiev	6.34
Moscow	6.37
ZONE 7	
Cape Town	7.04
Jakarta	7.16
ZONE 8	
Honolulu	8.13
Ottawa	8.24
Anchorage	8.39
ZONE 9	
Buenos Aires	9.05
Brasilia	9.24
Washington DC	9.38
V.A. Lab	9.46

Conference / Telepresence Room

ZONE 3	
Athlone	3.41

YOU ARE HERE

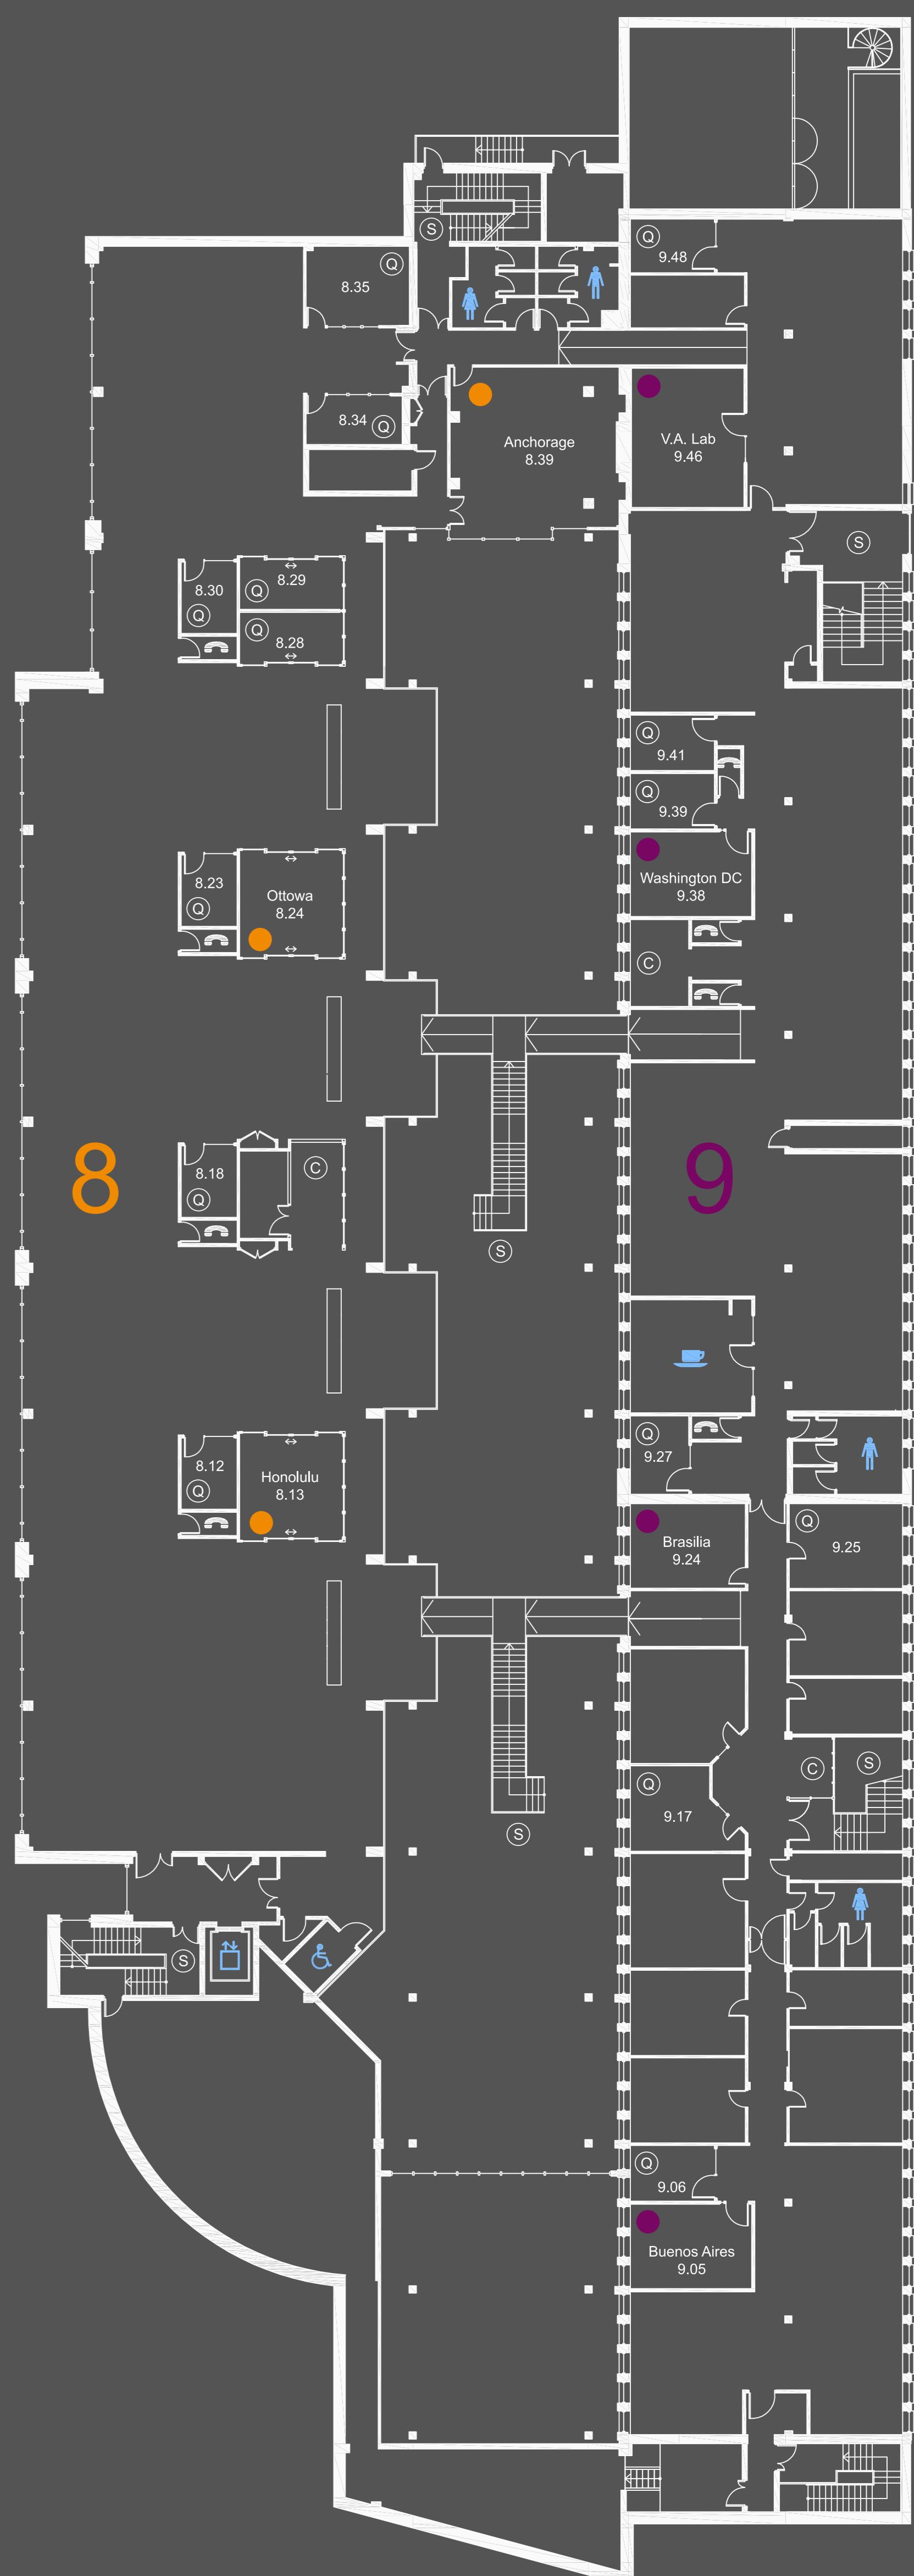


FIRST FLOOR

ERICSSON SOFTWARE CAMPUS




GROUND FLOOR

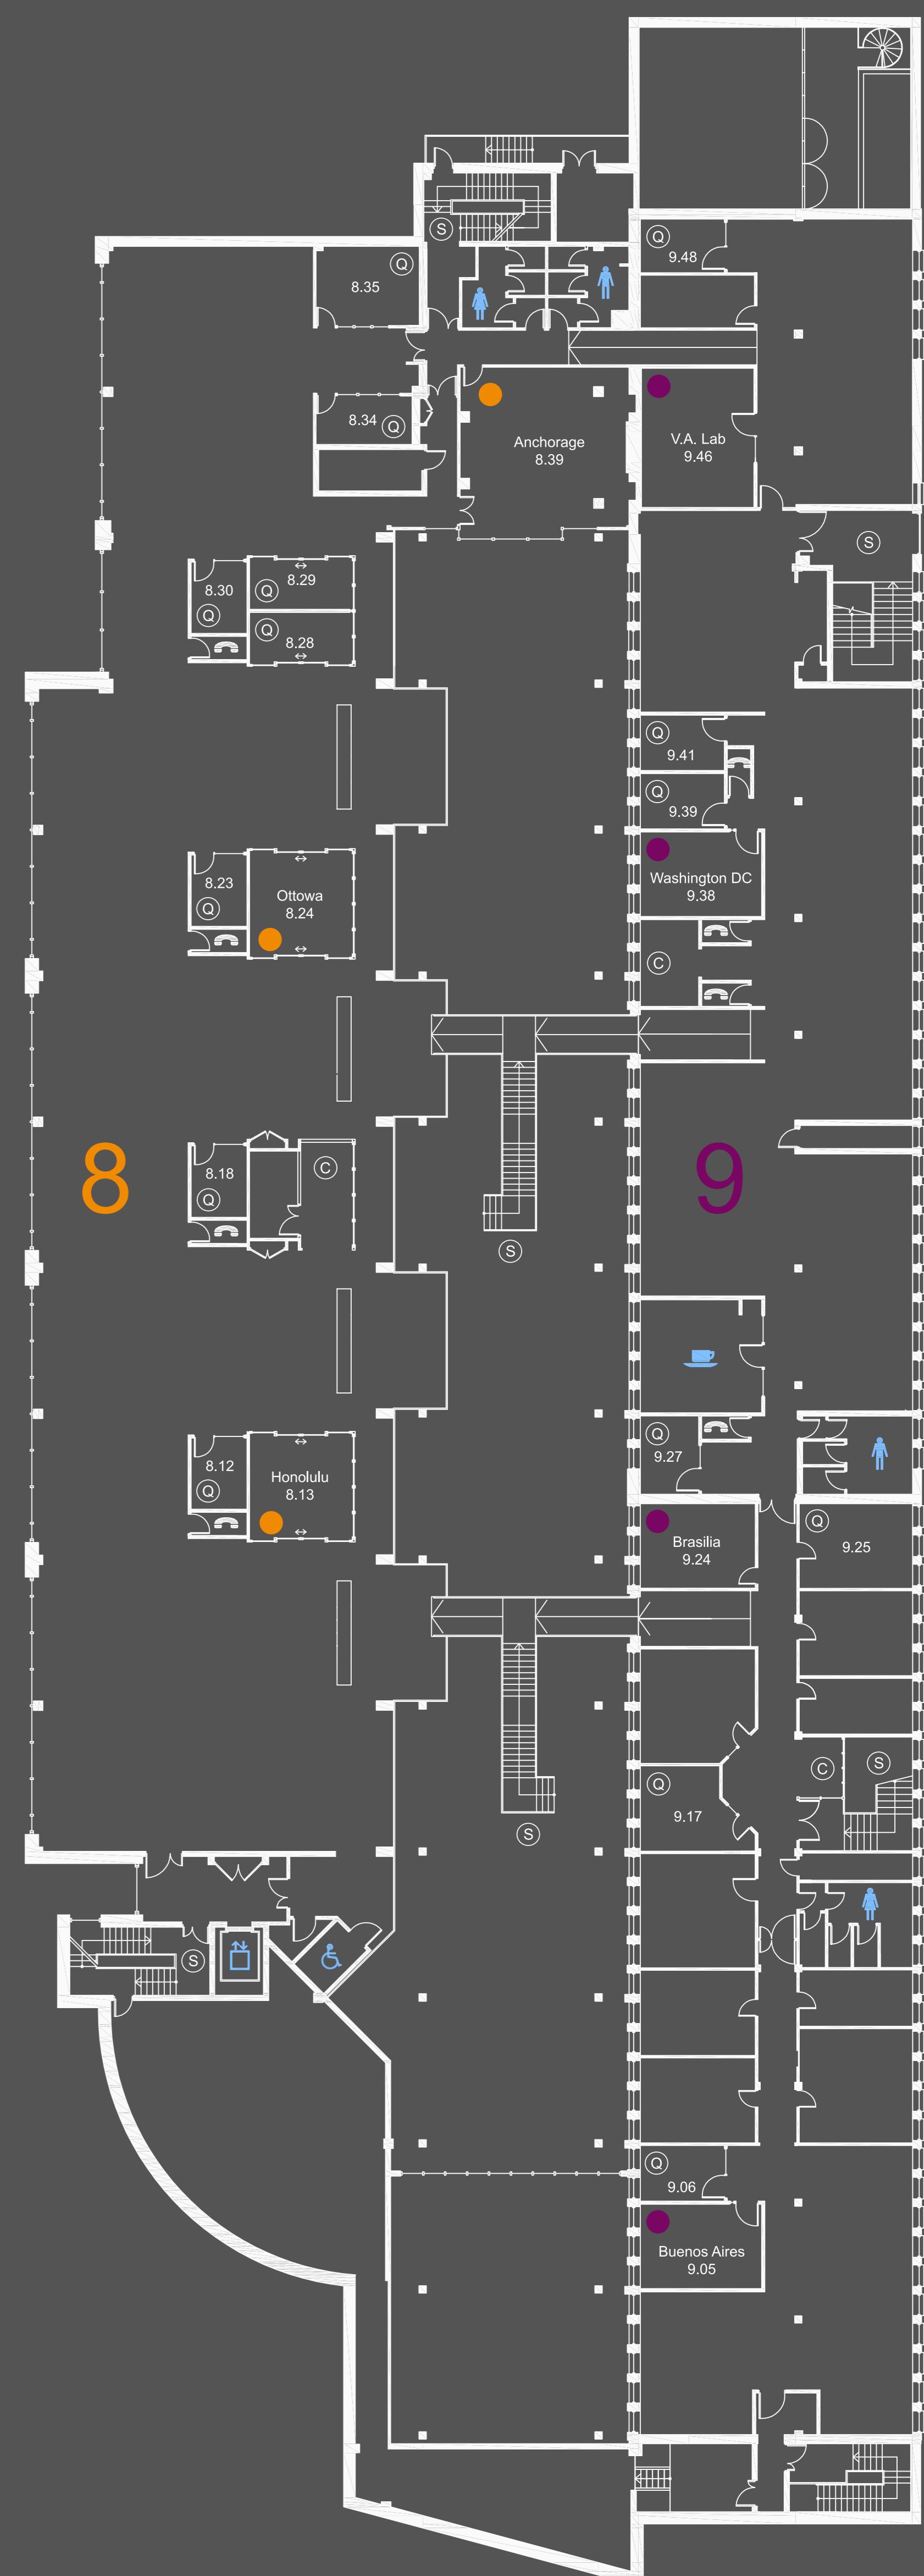

FIRST FLOOR


ERICSSON SOFTWARE CAMPUS

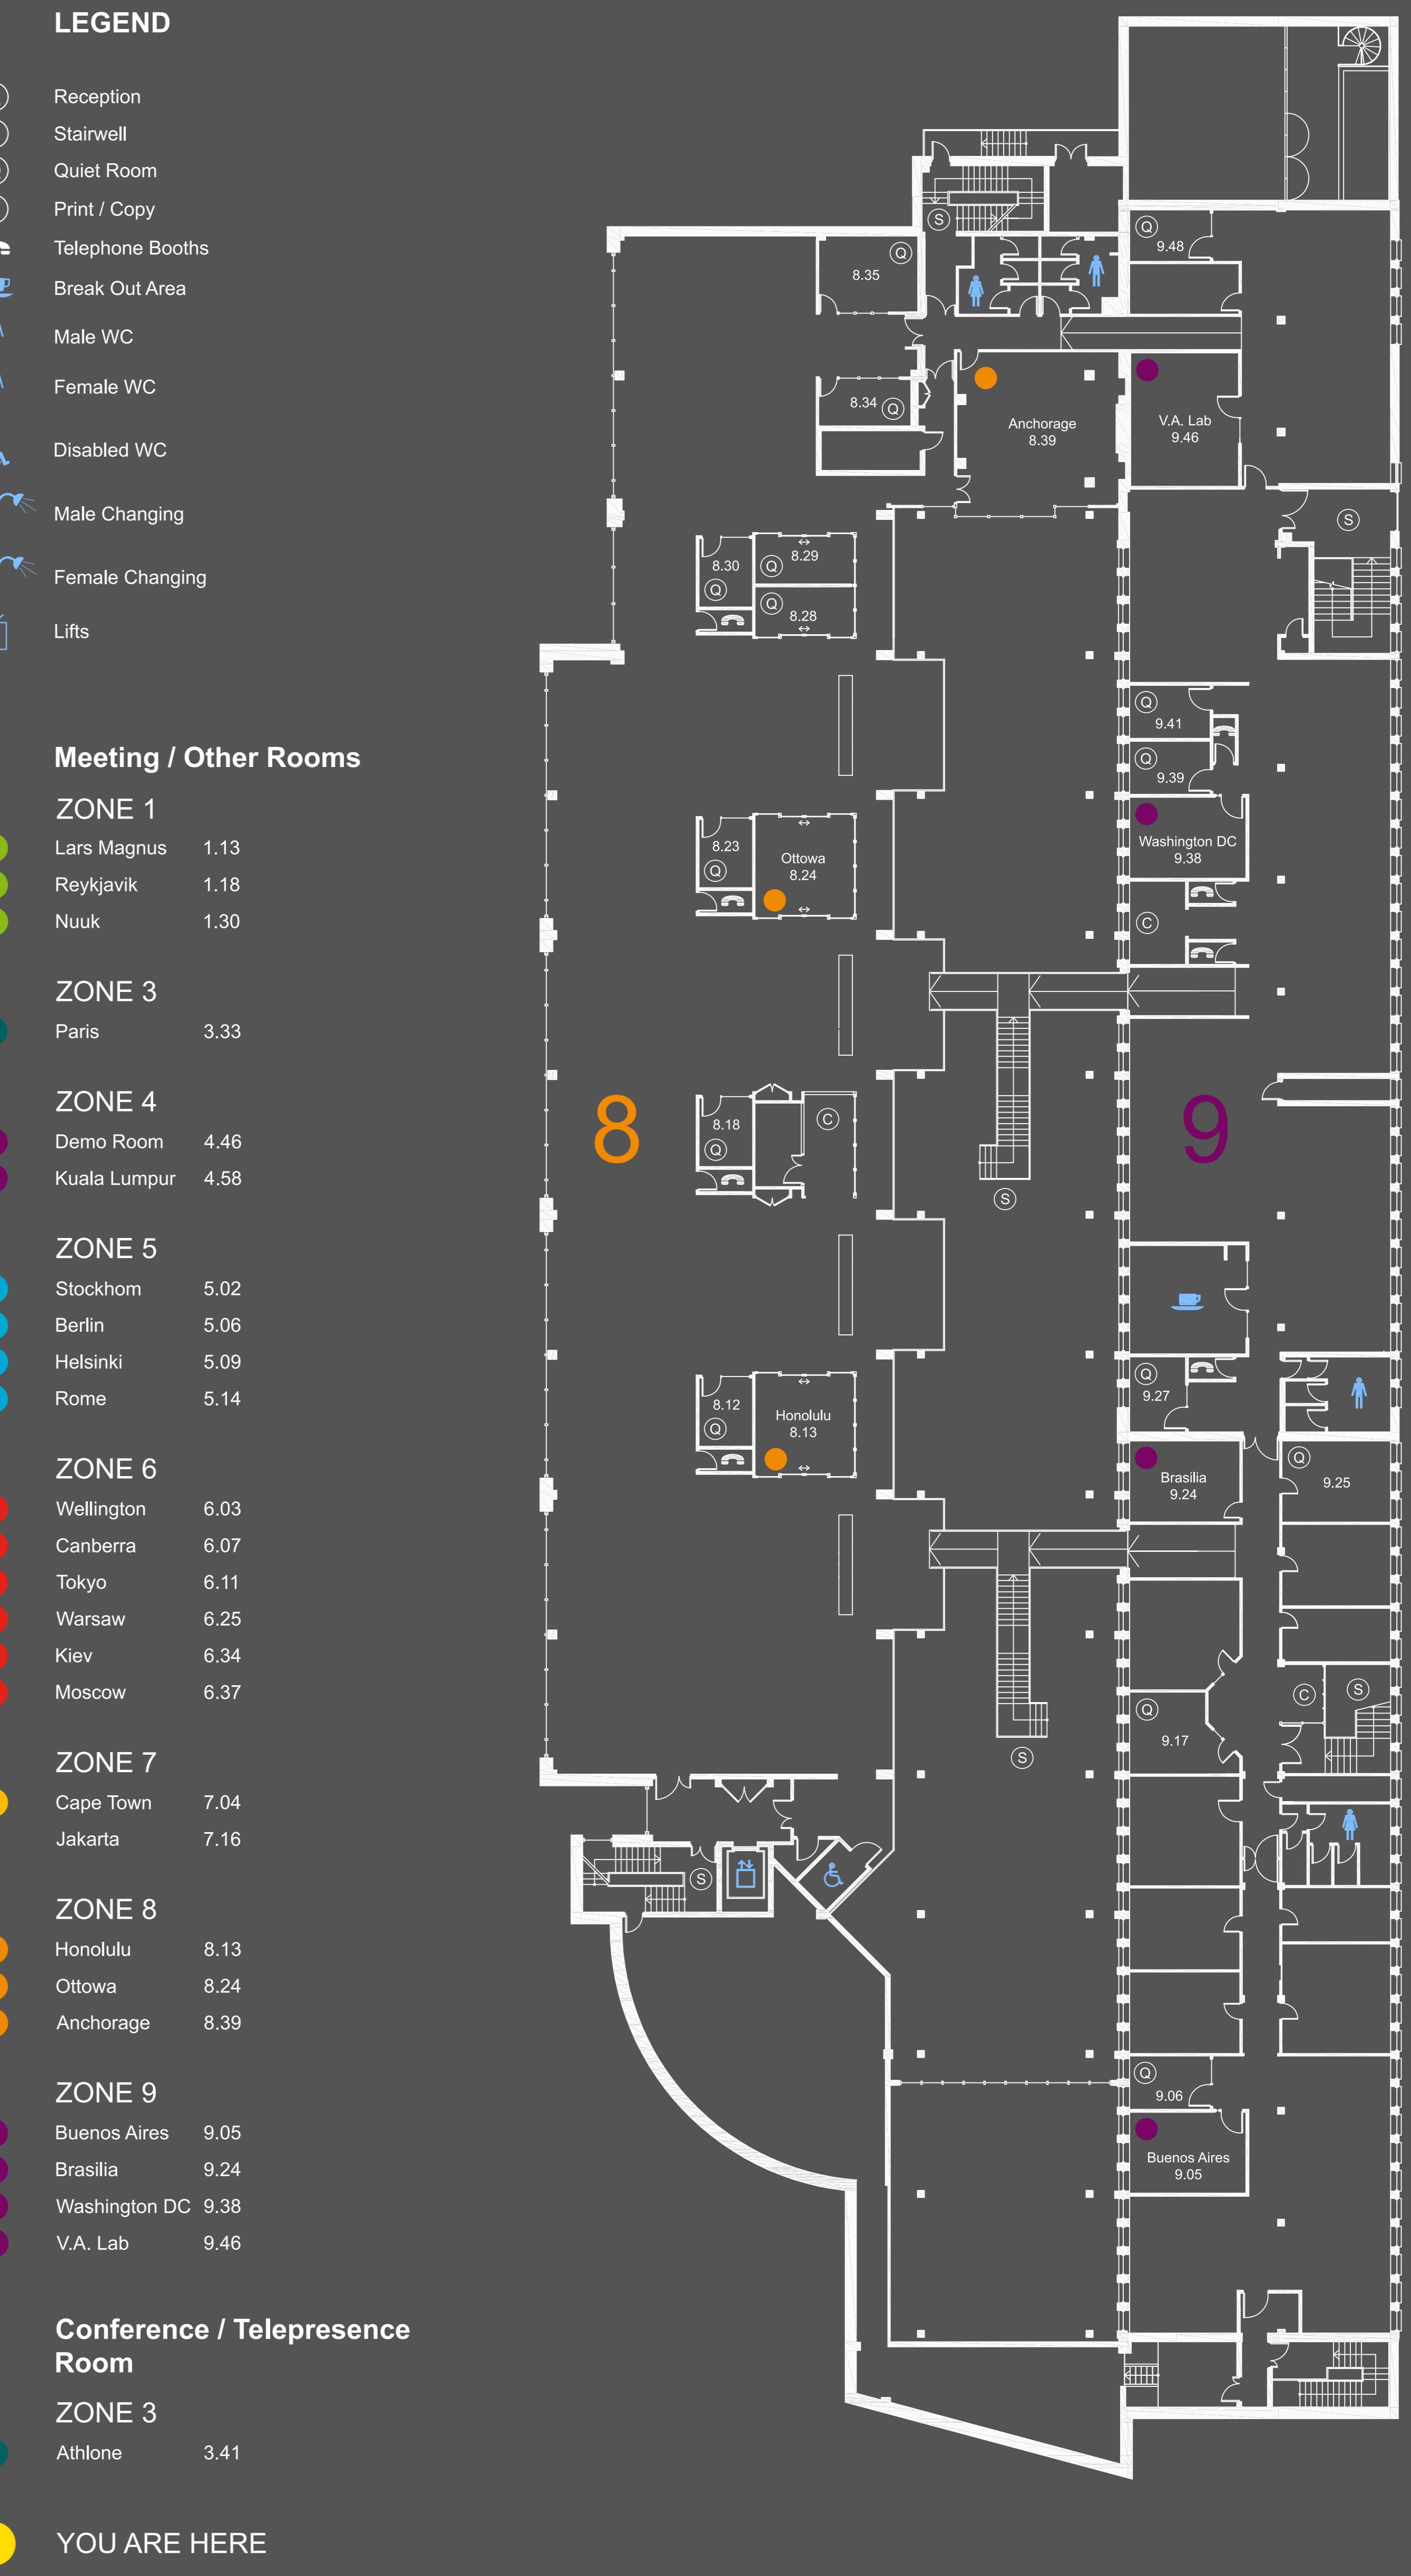

ERICSSON SOFTWARE CAMPUS




GROUND FLOOR

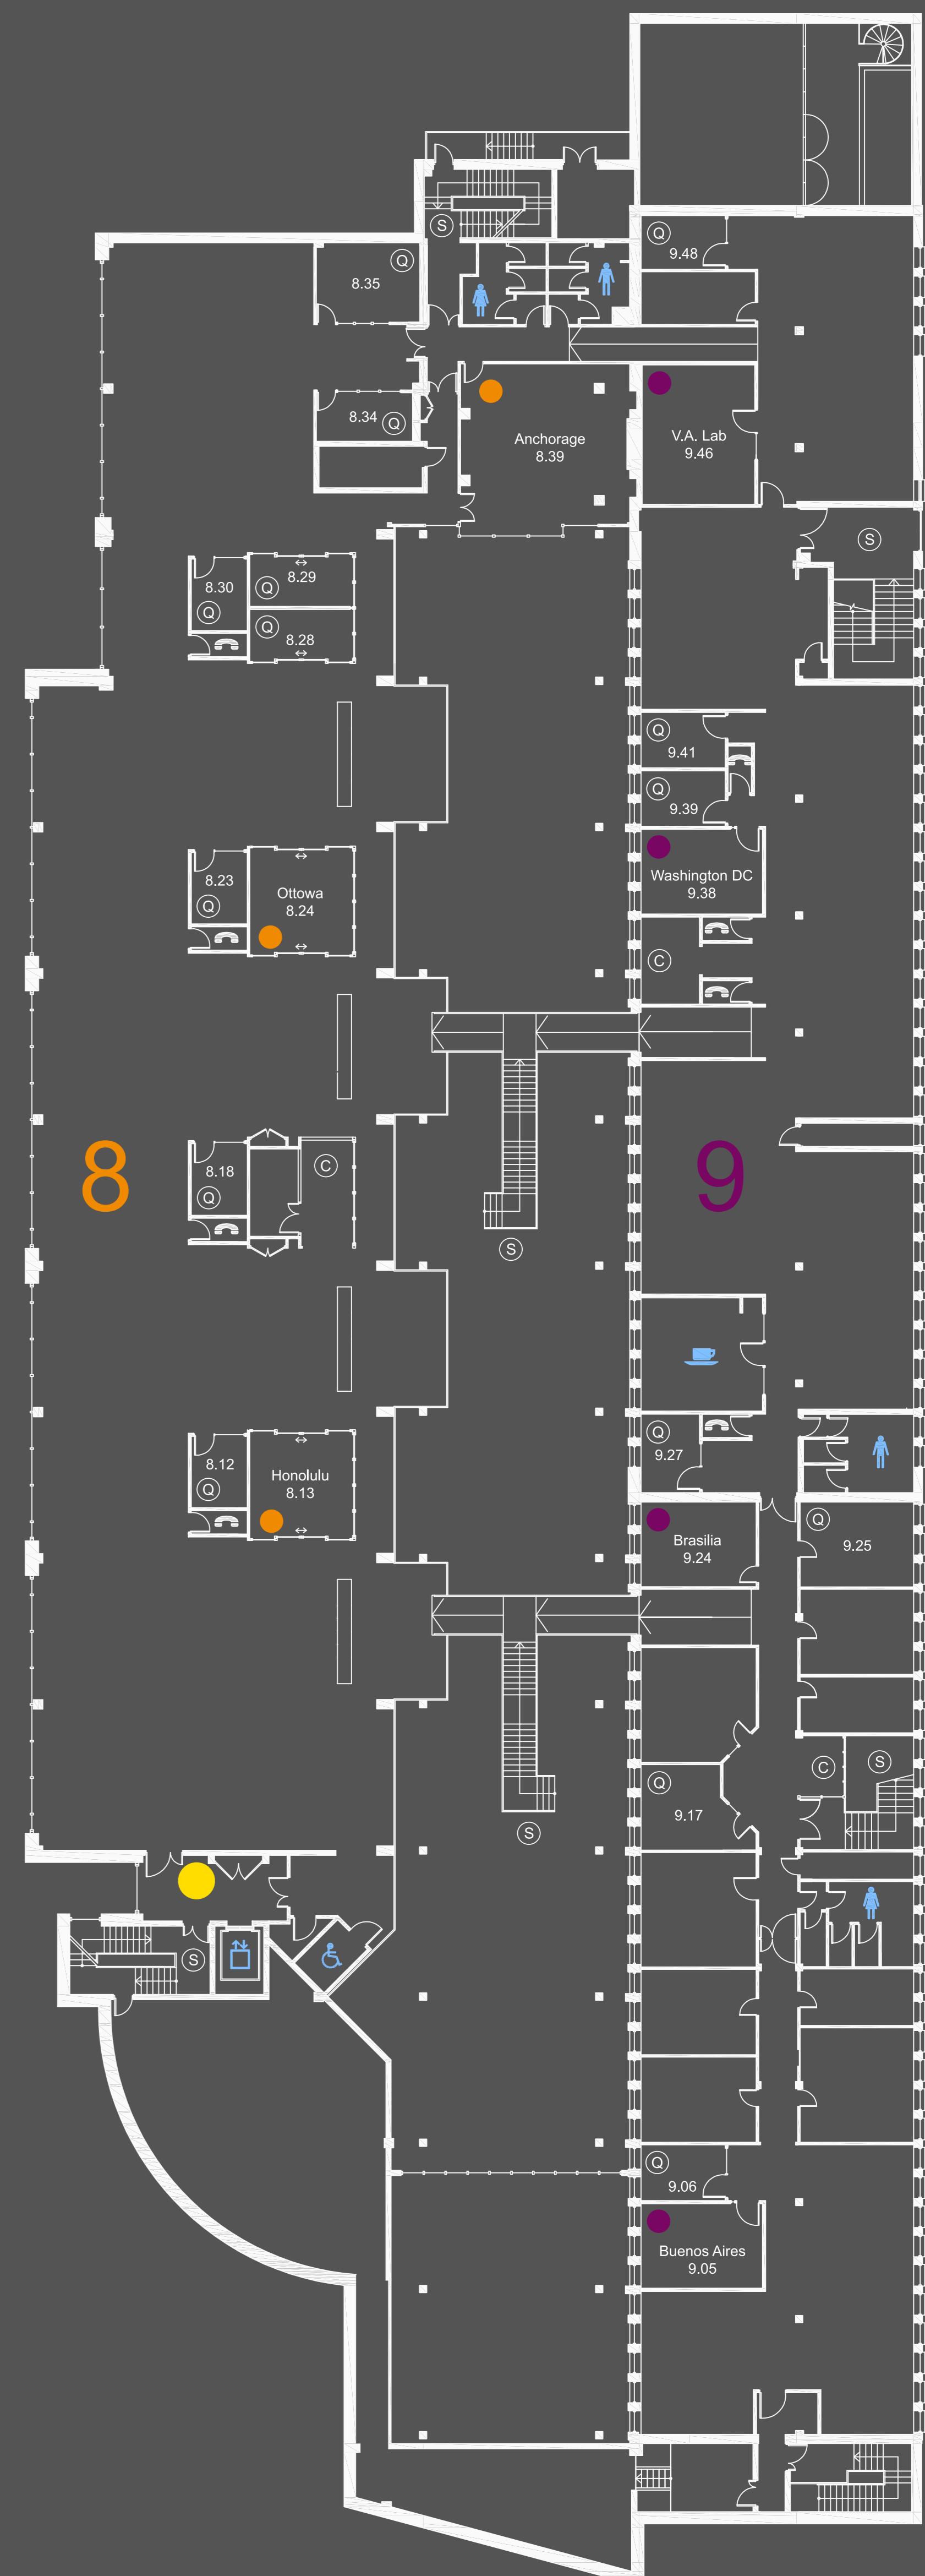

FIRST FLOOR


ERICSSON SOFTWARE CAMPUS

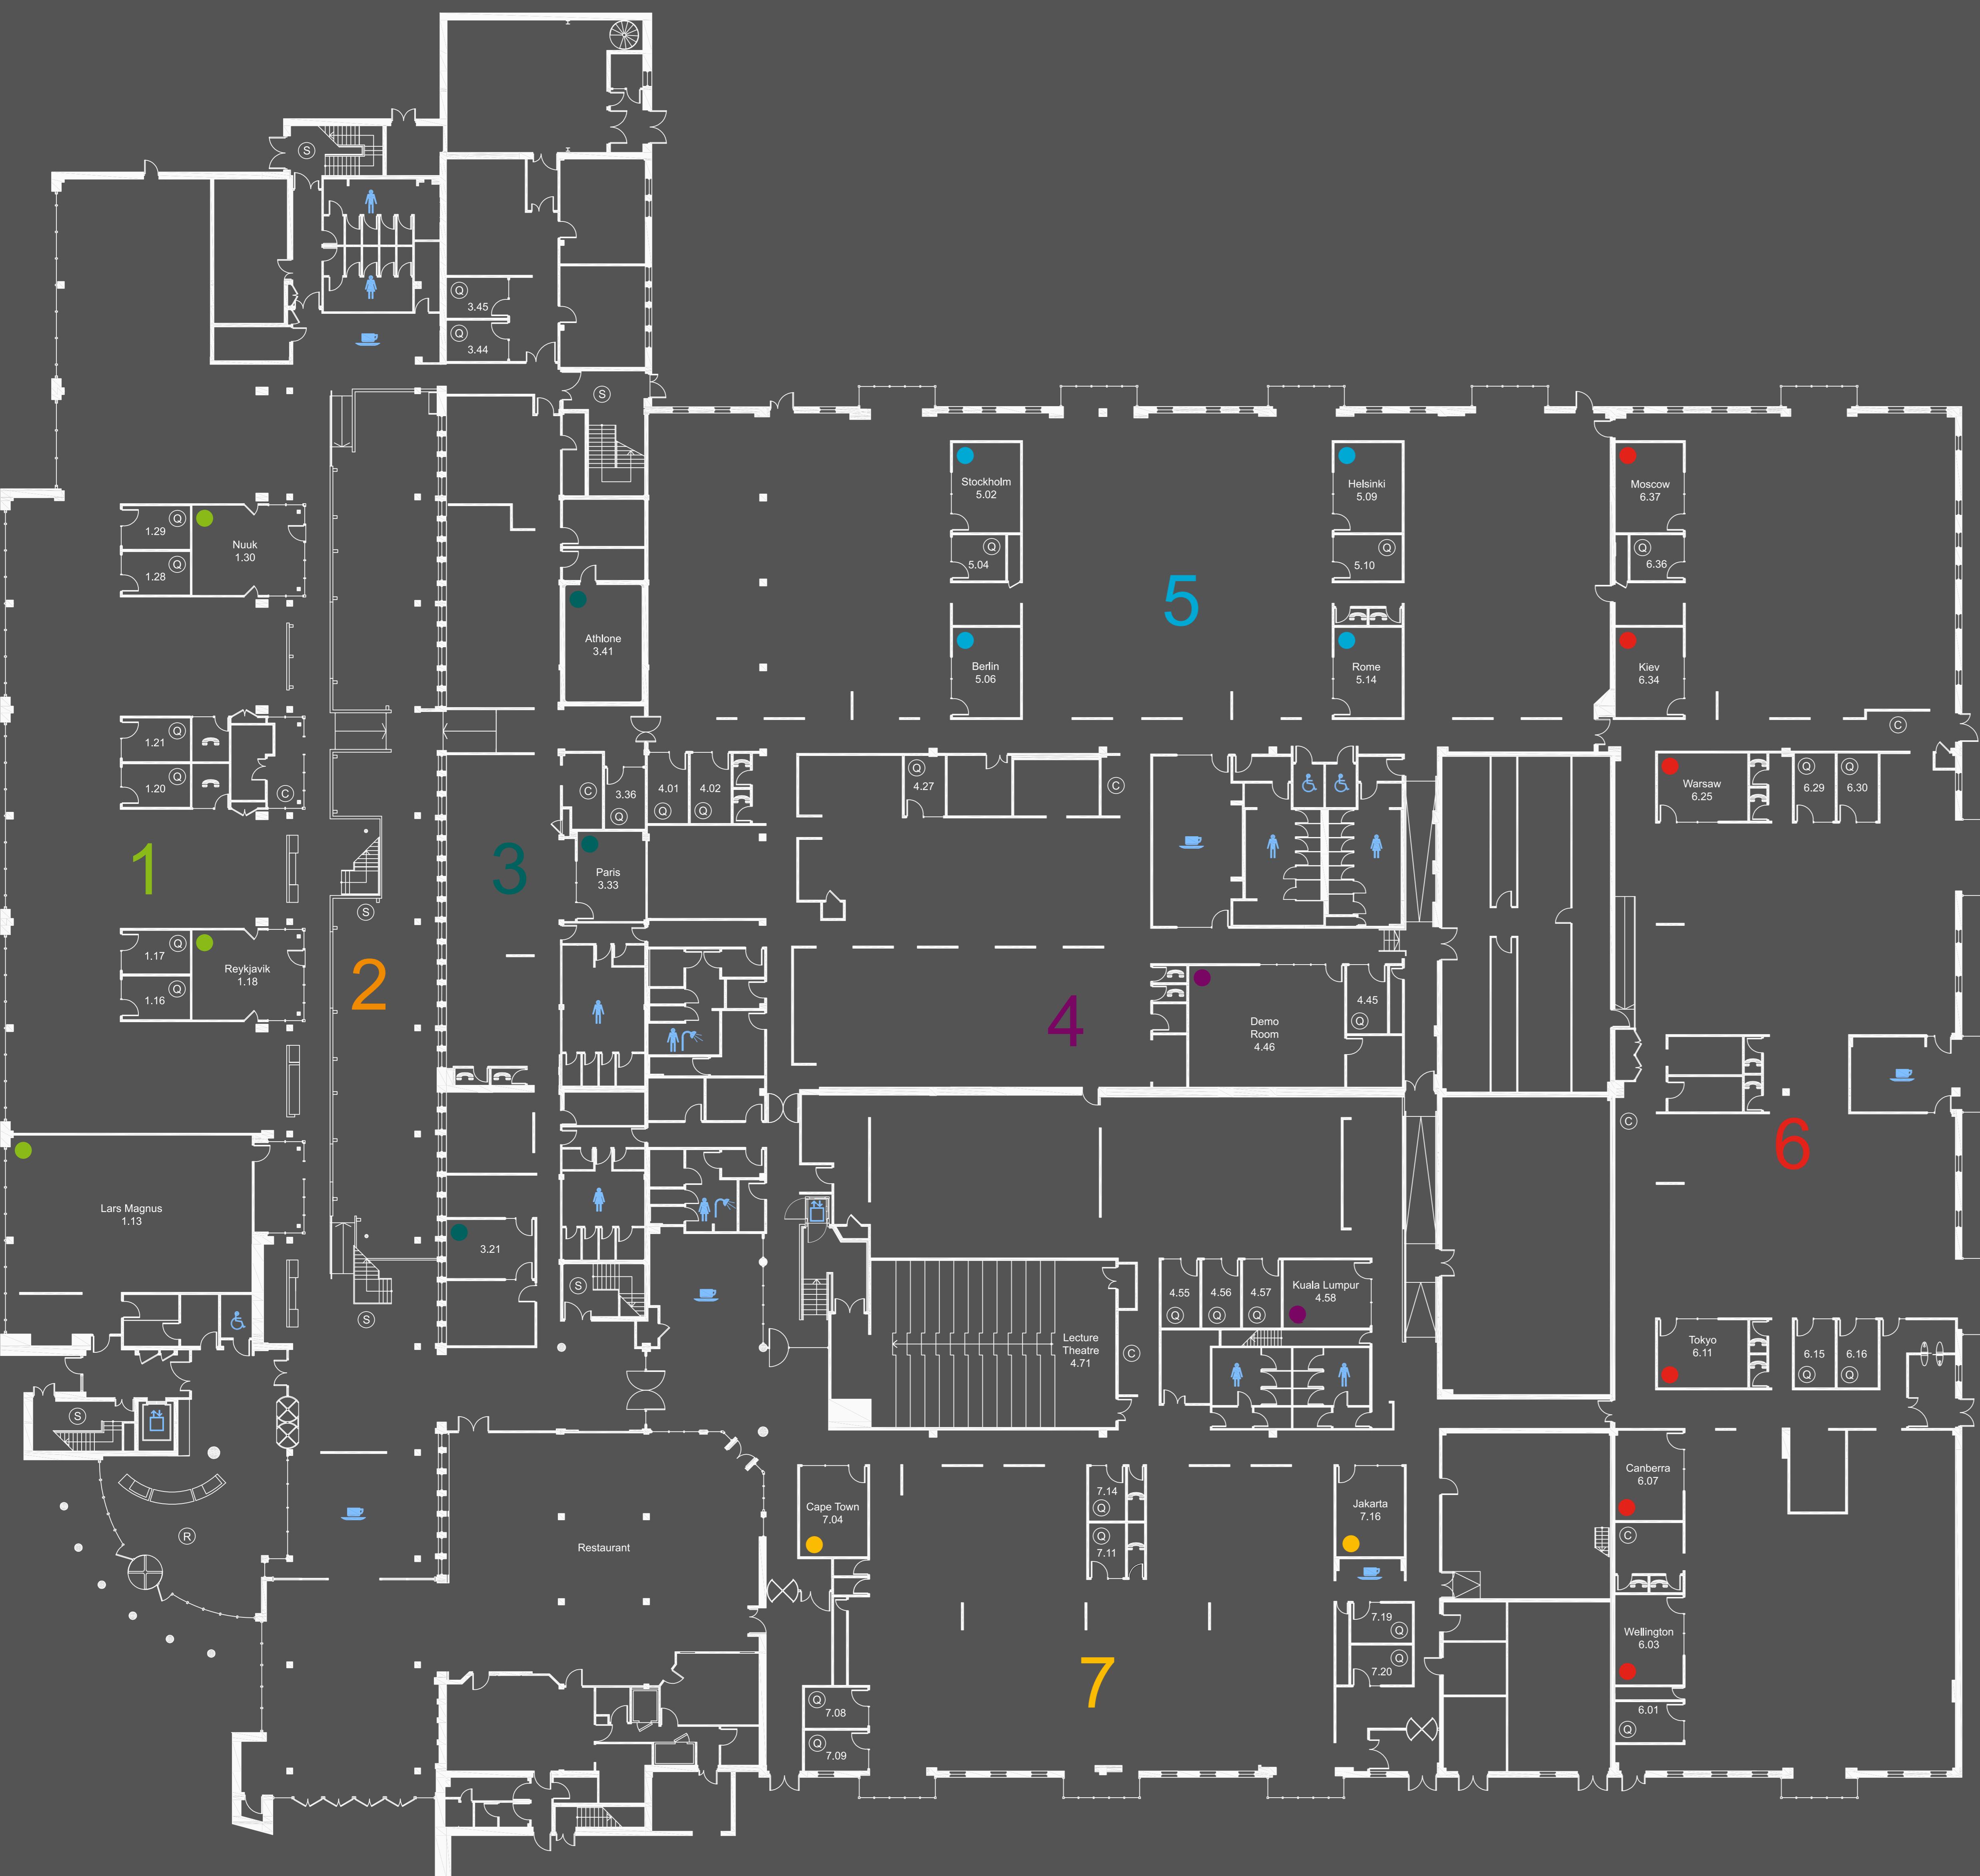

GROUND FLOOR



YOU ARE HERE

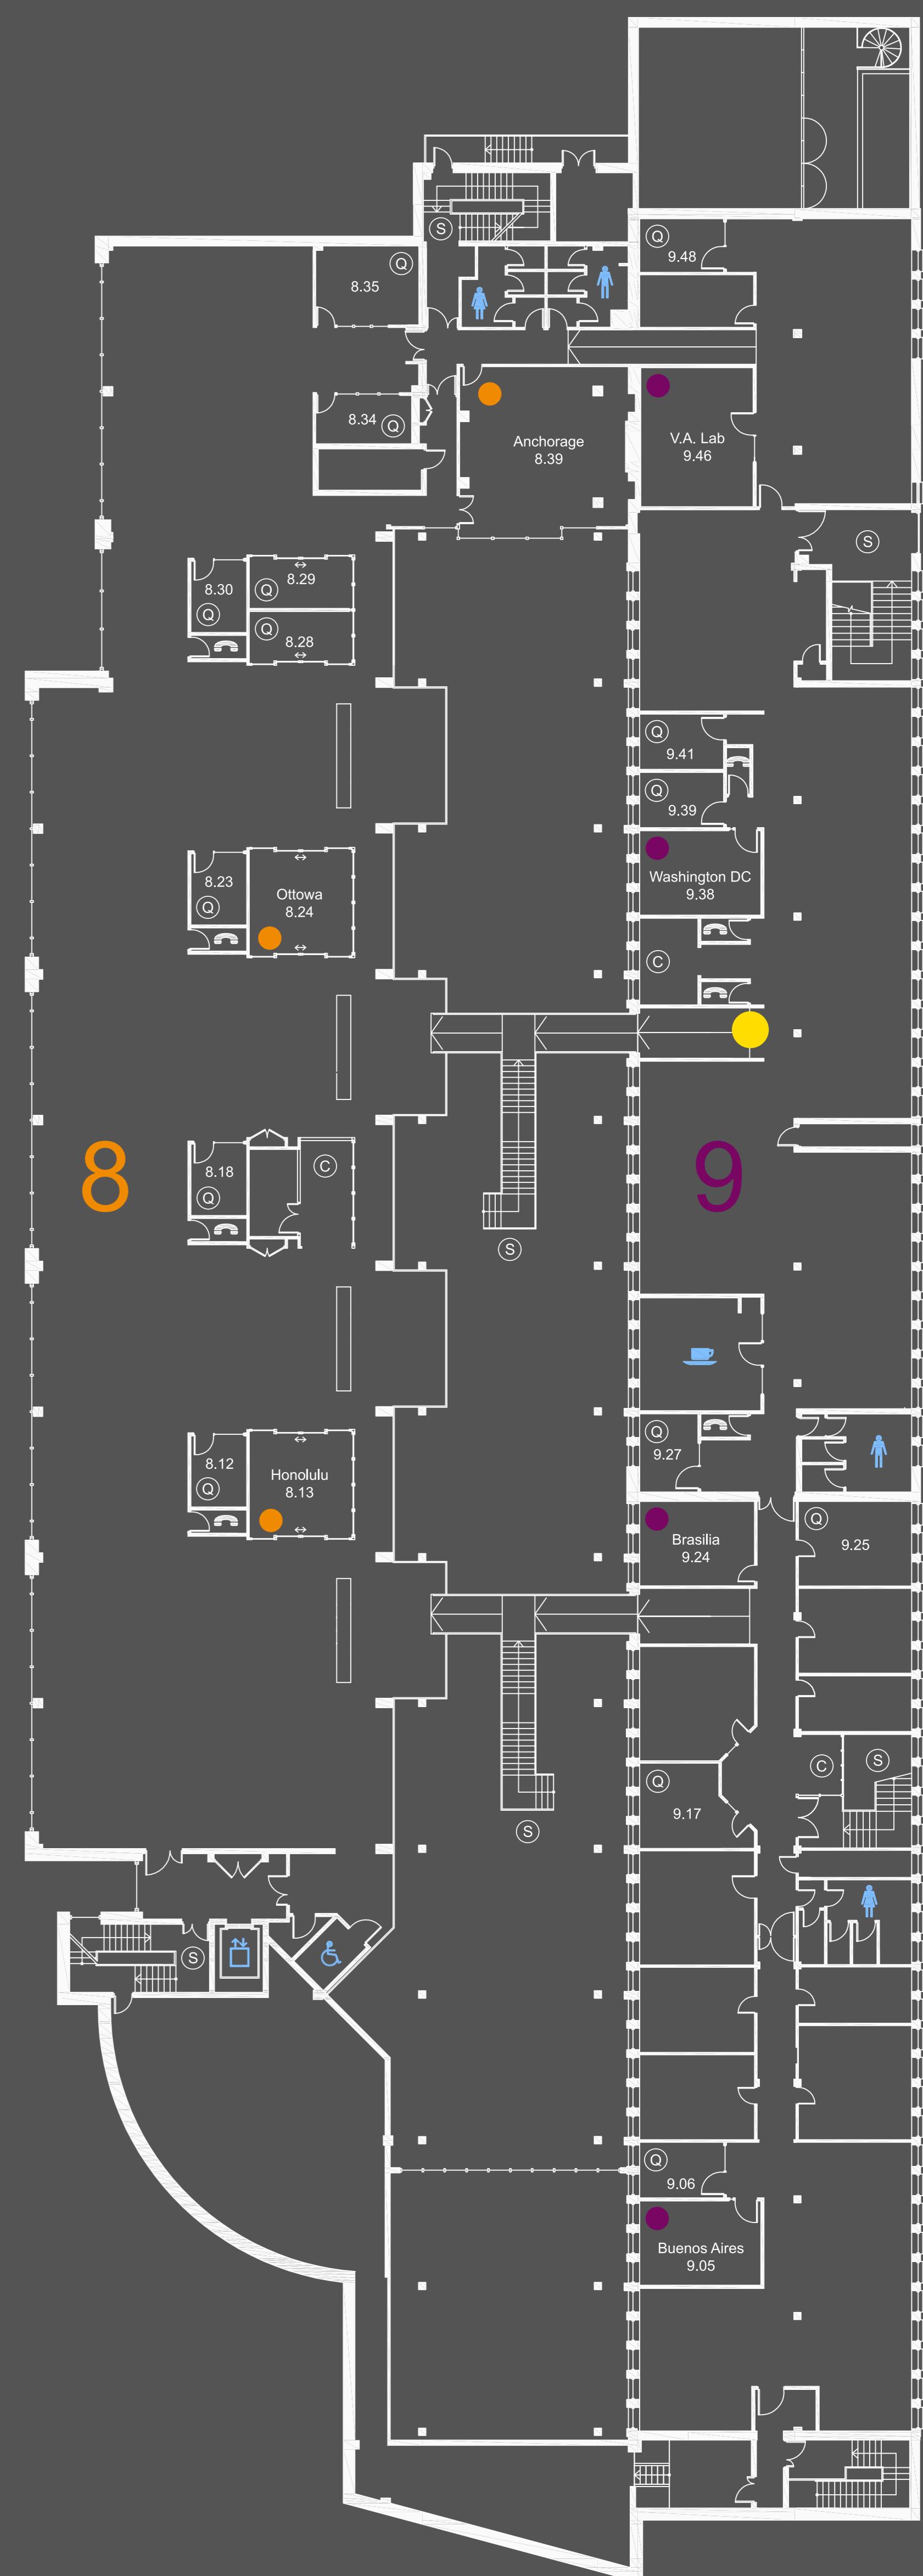

FIRST FLOOR


ERICSSON SOFTWARE CAMPUS



GROUND FLOOR



YOU ARE HERE

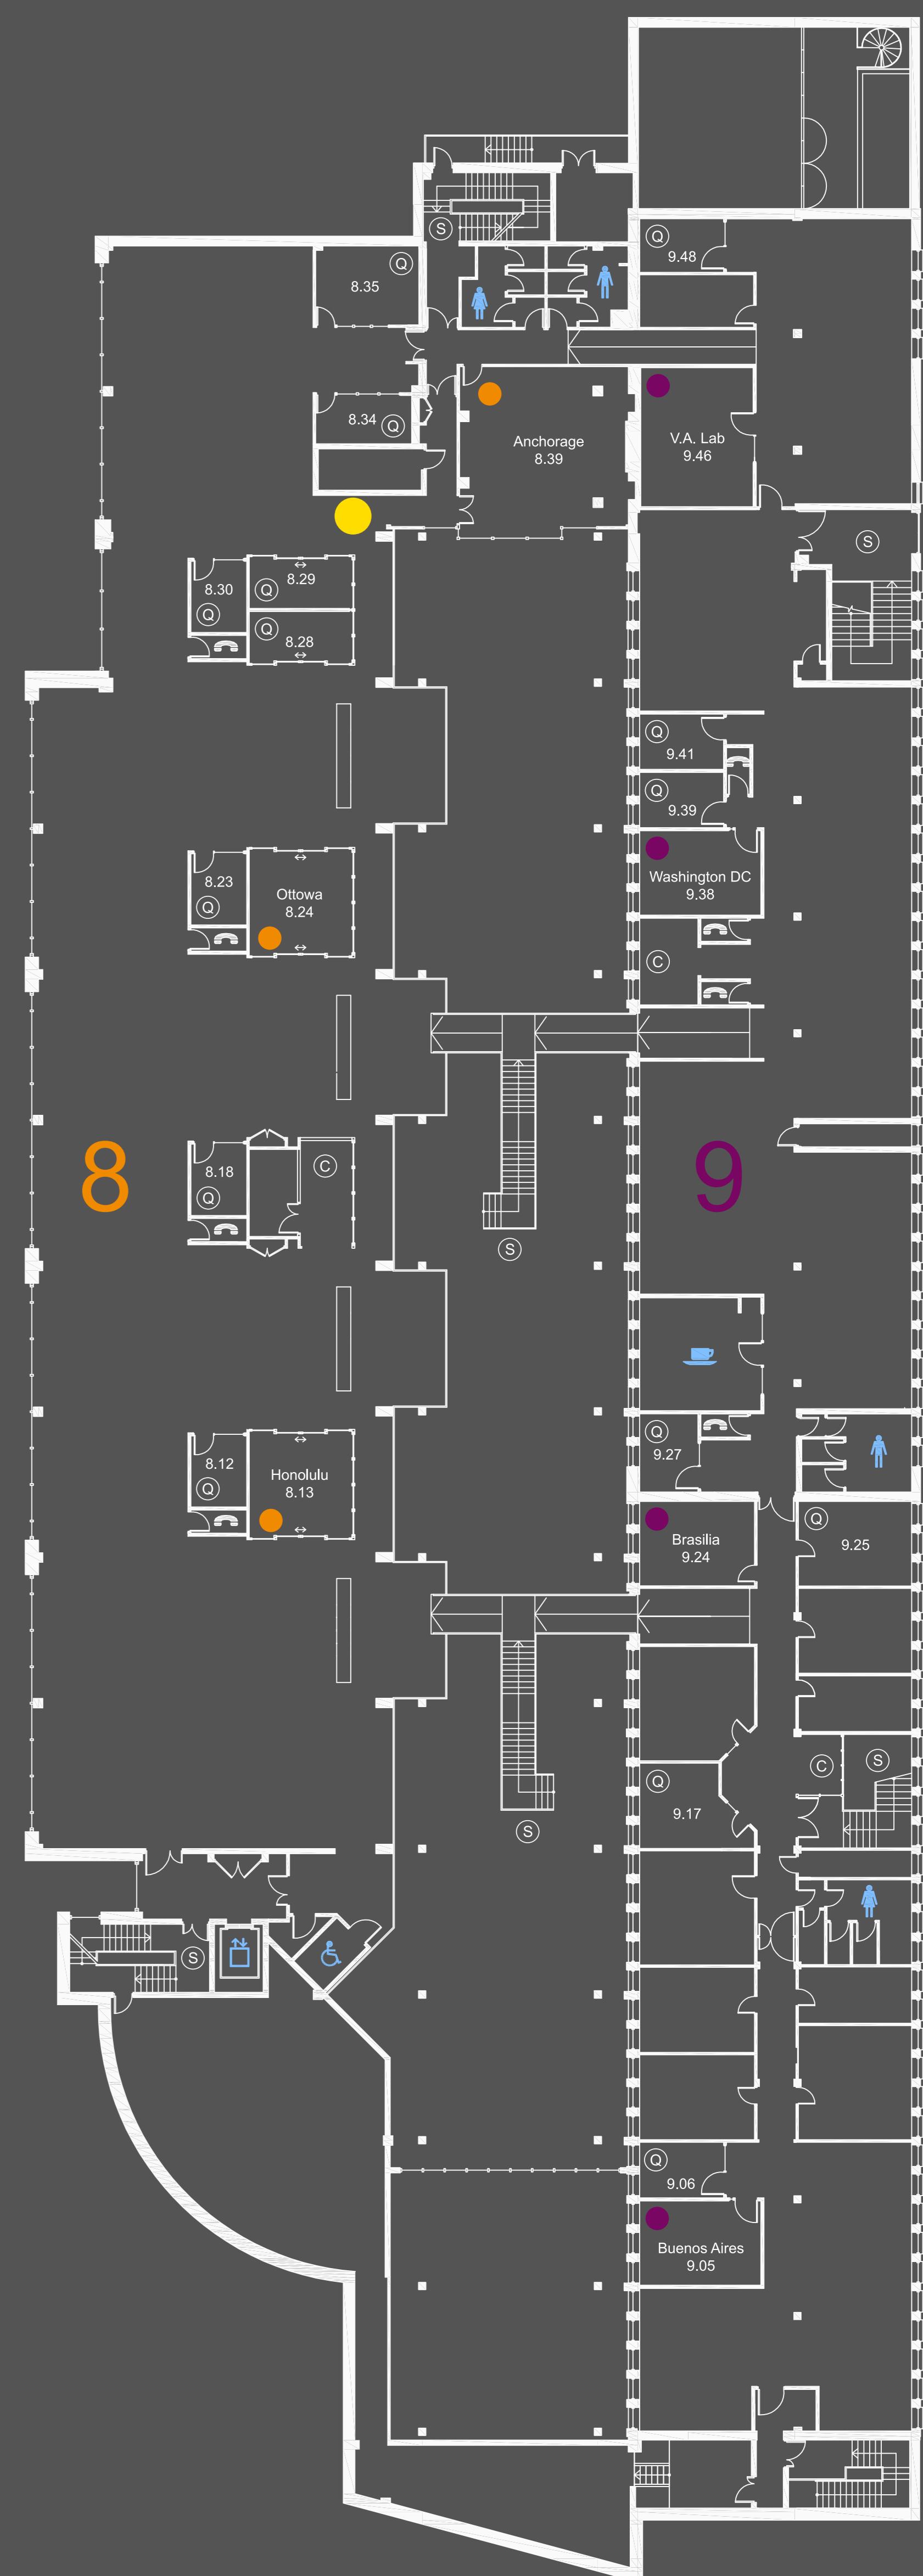

FIRST FLOOR